


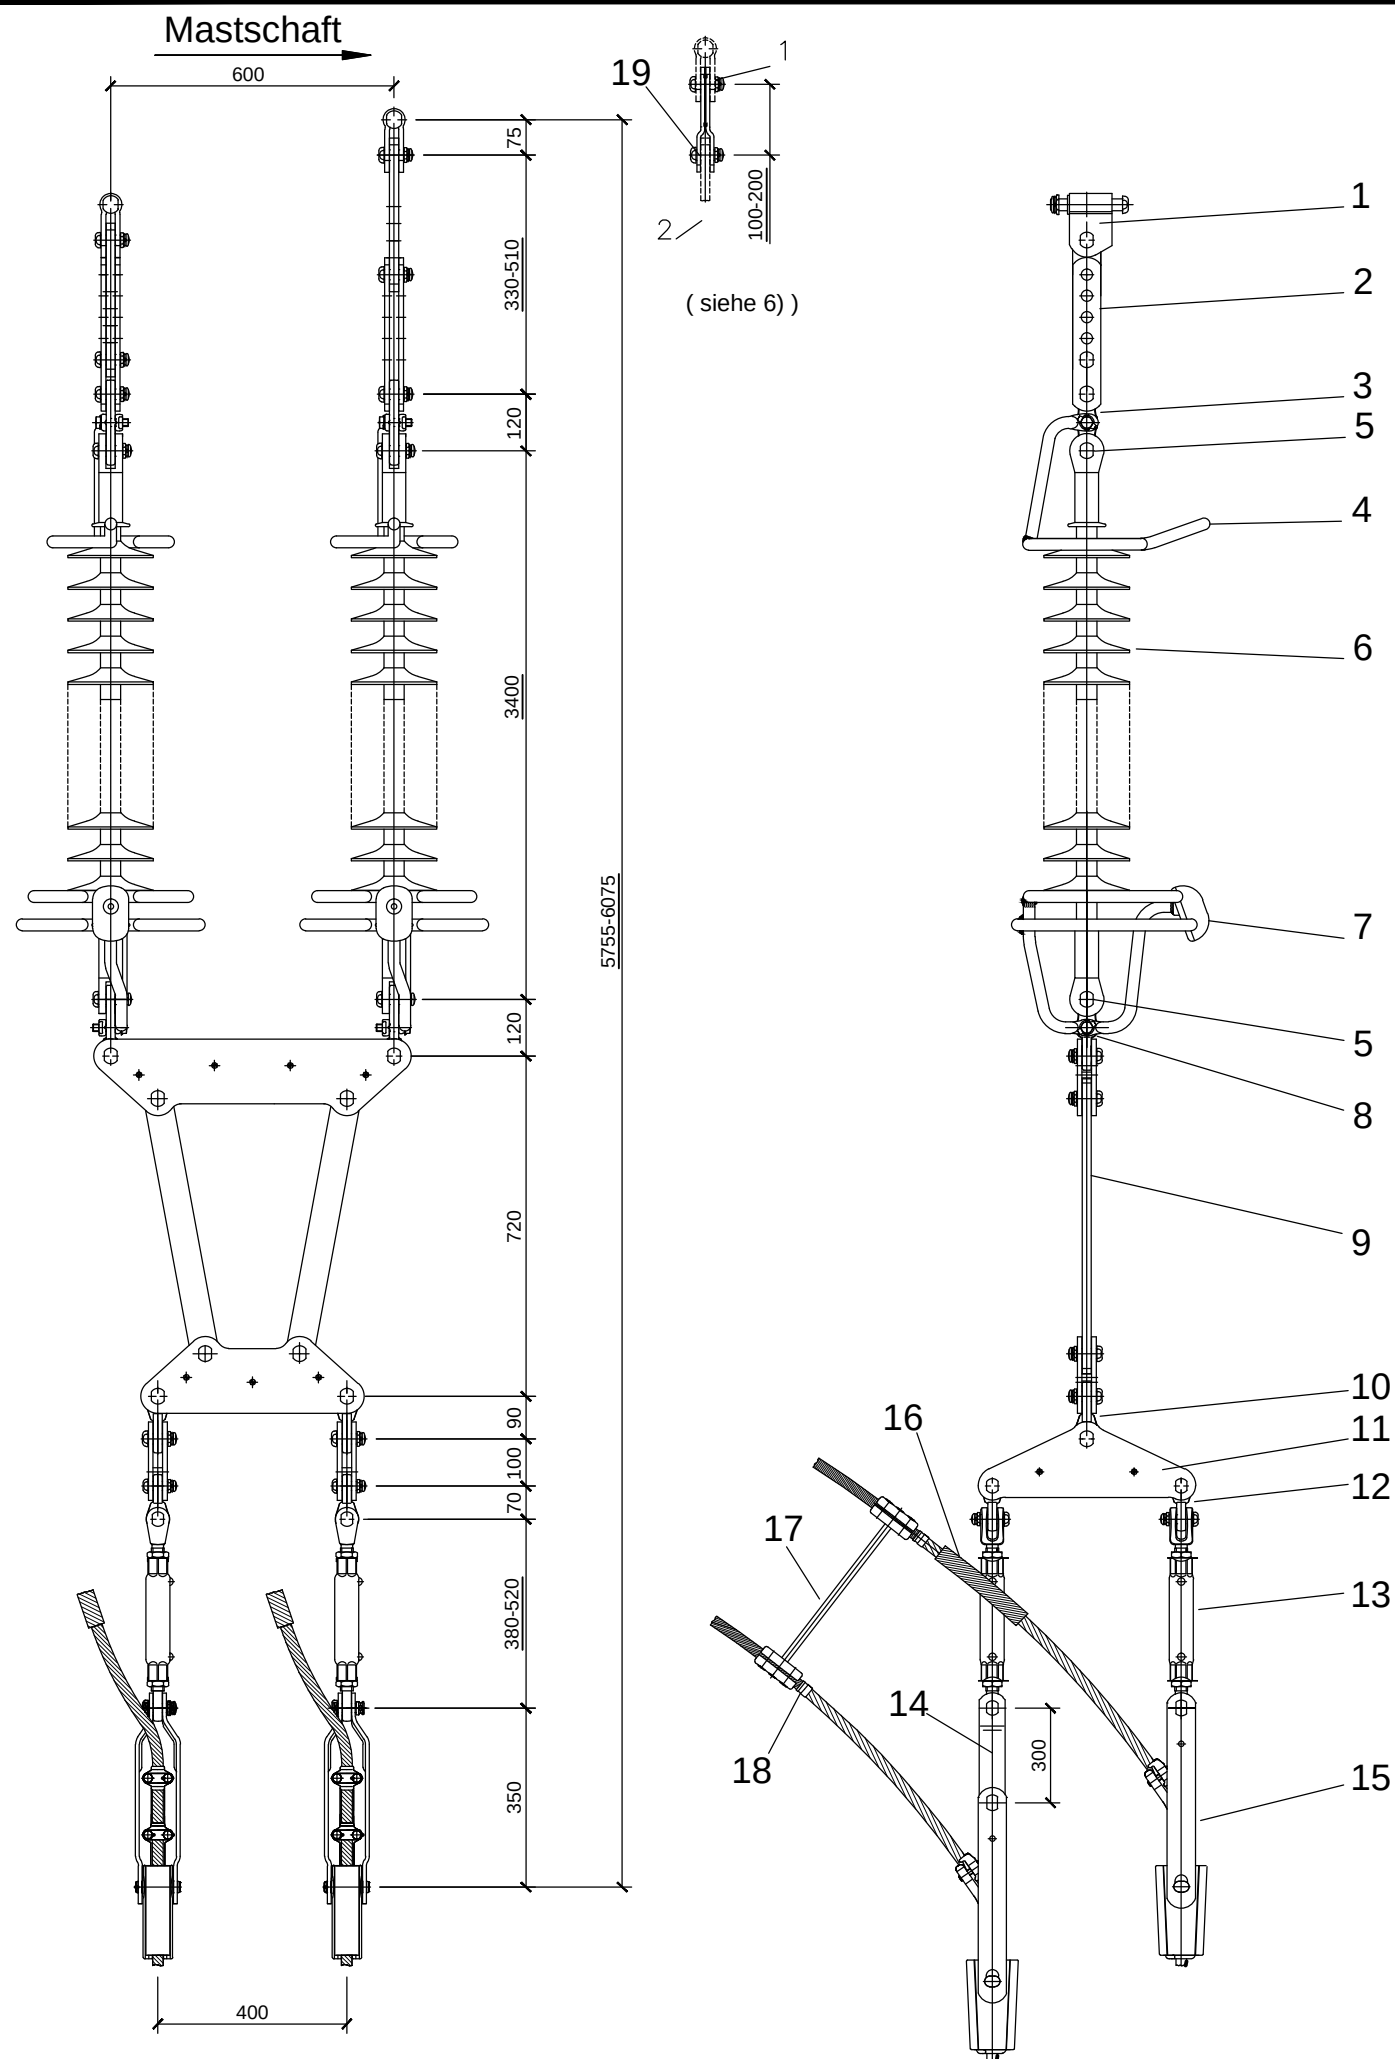

Stückliste

Pos. Nr.	Stück je Kette	Benennung	Nennkraft in kN	SAP-Nummer
1	2	Abspanngelenk DIN 48066 BS 25x130...230-22-100...200 5)	280	siehe Liste
2	2	Noniuslasche S22-24 BH: 330-510	280	52224151
3	2	Doppelöse DIN 48069-C22 BH:120 SAB	280	52219355
4	2	Schutzring Einhorn Verbund oben BH:270	-	52201011
5	4	Verbindungsbolzen DIN 48073 S22x57-8.8	-	52232622
6	2	Isolator Verbund CS260 8400/3400 S22	260	52105309
7	2	Schutzring Tandem Verbund unten BH:300	-	52201012
8	2	Doppelöse DIN 48069-D22 BH:120 SAB	280	52219455
9	1	Abspanngarnitur S22 600x400x720 Trapez	550	52226217
10	2	Doppelöse B22 BH:90	280	52219246
11	2	Abstandhalter AS 19-22-400x100 3eck	280	52225577
12	4	Doppelöse DIN 48069-B19 BH:70	200	52219213
13	4	Spannschloß DIN 48334 AB19 M24x380-520	200	52224705
14	2	Gabelllasche DIN 48078-AS-S19-20 BH:300	200	52223415
15	4	Keilabspannklemme S19 21,8-22,5	170	52303008
16	2	Reparatur-Spirale 21,60-22,50 L: 500 mm	-	52321528
17	2	Stromschlaufendistanzhalter 4-BDL 21,1 - 23,4	-	52313319
18	4	Endhülse 22,3-22,8 AL(für Leiter 264-AL1/34-ST1A) Endhülse 21,7-22,2 AL(für Leiter 243-AL1/39-ST1A)	-	52312309 52312308
19	1	Gabelllasche DIN 48078-AS-S22-24 BH: 100...200 6)	280	siehe Liste
20		Feldabstandhalter 4-BDL 20,9-22,4 SD 7)	-	52314009

Mechanische Werte

Kettengewicht:	ca. 200 kg
Kettenlänge:	ca. 6000 mm
Kettenfläche :	ca. 0,6-0,7 m ²
Leiter/ σ +10°C	4x264-AL1/34-ST1A / 46 $\frac{N}{mm^2}$ 4x243-AL1/39-ST1A / 48 $\frac{N}{mm^2}$
Eiszone / Windzone:	E2/W2
Gewichts-/Windspannweite :	650/500

Elektrische Werte

Nennkurzzeitstrom:	40 kA
Schlagweite:	2950 mm
Isolator:	Verbund-Langstabisolator
Ausführungsform:	CS260 C22L 1675/8400/3400
Kriechweg:	8400 mm
Verschmutzungsgrad:	II nach DIN EN 60071-2

Beachtung bei der Montage / Mengenermittlung

- Verbindungsbolzen : Mutter und deren Sicherungen zum Mastschaft, zur niedrigeren Mastnummer oder nach unten
- Brennstrebe : nach oben
- Montage der Bauteile nach Herstellervorschrift
- Montage der A2/A4 - Schraubenverbindungen gefettet
- Pos. 1: Größe Abspanngelenk anpassen an Mastkonstruktion
- Pos. 19: Länge Gabelllasche anpassen an Winkelstellung. Bei Winkelabspannmasten mit Leitungswinkel < ca. 140° ist zum Winkelausgleich eine zusätzliche Gabelllasche zur Noniuslasche zu verwenden
- Pos. 20: Einbau und Anzahl gemäß Schwingungsstudie.

d.	16.02.2017	As	Spannschloß von M27 auf M24 angepasst			
Index	Rev.-Datum	Gez.	Änderung			
		Technische Ref. / Firma	Erstellt durch GSG-ECO Dorin	Genehmigt von AMG-ST-TL Dörr	Datum 11.07.2016 Erstelldatum 23.08.2007	Format A3
						Maßstab 1:16
		Objektname KETTEN . .				Zählteil
		Zugehörigkeit THN - REGELBAUWEISE 380-kV KETTEN			DCC EZ3	Status Gültig
Identnummer 000-885-889		Titel 380-kV DA-Kette Verbund, CS260, VGII 4x264-AL1/34-ST1A und 4x243-AL1/39-ST1A, E2/W2				Eigennummer
						Fremdnummer