


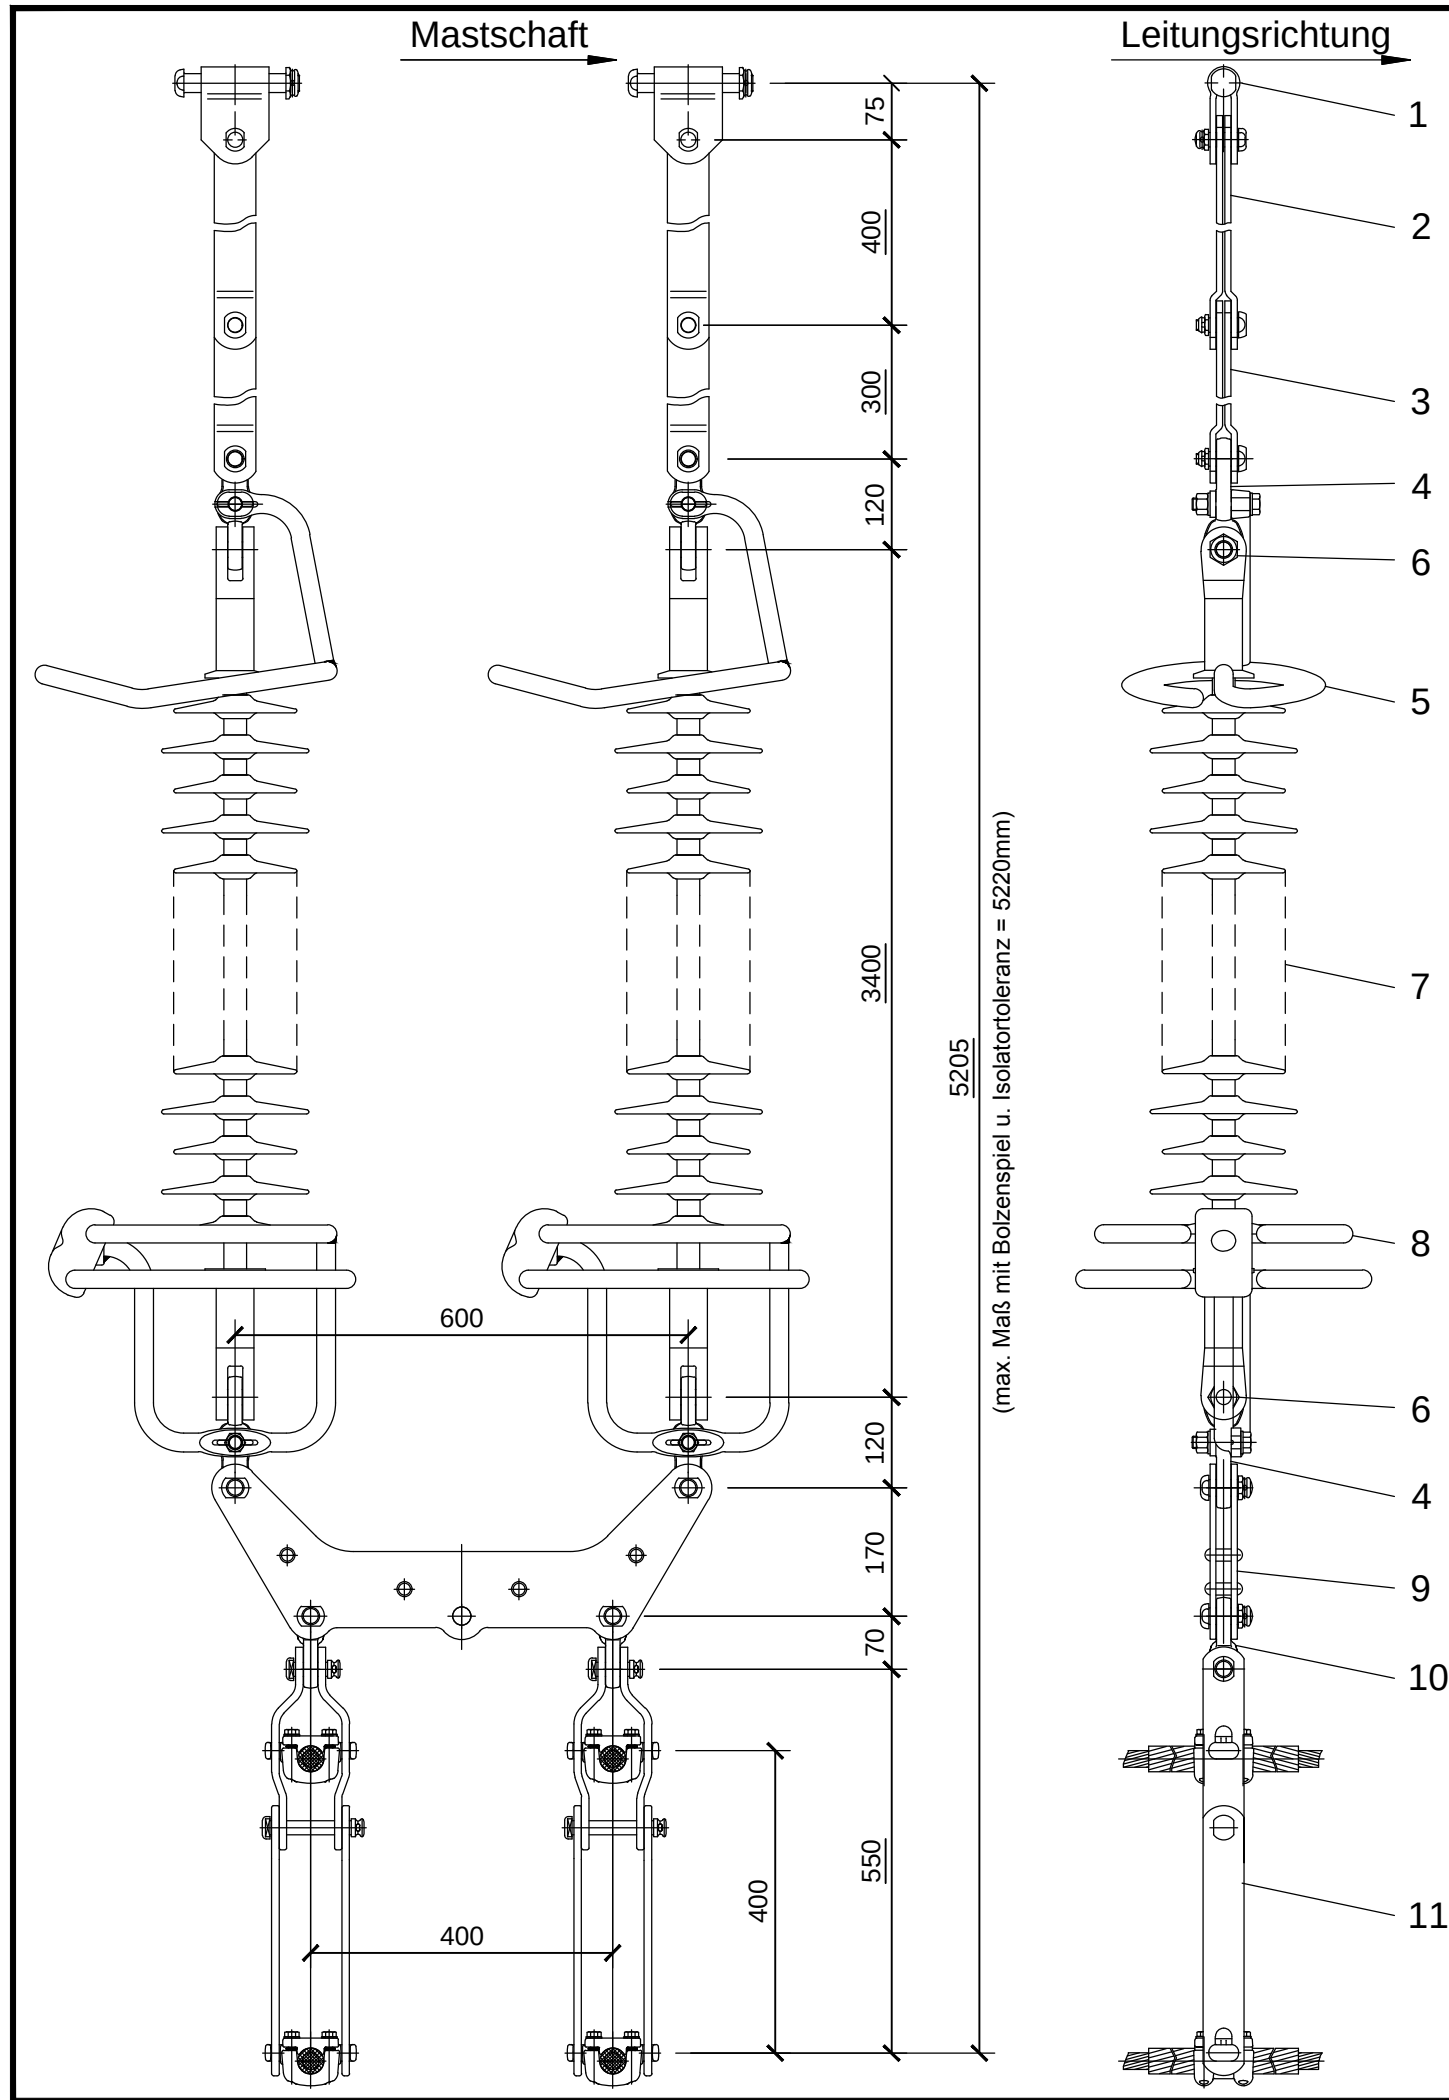

Stückliste

Pos. Nr.	Stück je Kette	Benennung	Nennkraft in kN	SAP - Nummer
1	2	Traggelenk DIN 48066 AS 25x130-19-100 (siehe 5)	200	52231510
2	2	Gabellasche DIN 48078-AS-S19-20 BH:400 (siehe 7)	200	52223417
3	2	Gabellasche DIN 48078-AS-S19-20 BH:300 (siehe 7)	200	52223415
4	4	Doppelöse DIN 48069-D19 BH:120 SAB	200	52219408
5	2	Schutzring Einhorn Verbund oben BH:270	-	52201011
6	4	Verbindungsbolzen DIN 48073 S19x48-8.8	-	52232604
7	2	Isolator Verbund CS 160 8400/3400 S19	160	52105323
8	2	Schutzring Tandem Verbund unten BH:300	-	52201012
9	1	Abstandhalter BS19-19-600x400x170 Trapez	240	52225914
10	2	Doppelöse DIN 48069-B19 BH:70	200	52219213
11	2	Spiraltragklemme S19 2-BDL 21,72-22,67	2x120	52301604
-	-	Feldabstandhalter 4-BDL 20,9-22,4 SD (siehe 6))	-	52314009

Mechanische Werte

Kettengewicht:	ca. 120 kg
Kettenlänge:	ca. 5210 mm
Kettenfläche :	ca. 0,4-0,5 m²
Ausschwingwinkel :	ca. 45 - 55° je nach Pos. 2 u. 3
Leiter/ σ :	4x264-AL1/34-ST1A / 46 $\frac{N}{mm^2}$ 4x243-AL1/39-ST1A / 48 $\frac{N}{mm^2}$
Eiszone / Windzone:	E2/W2
Gewichts-/Windspannweite :	650/500

Elektrische Werte

Nennkurzzeitstrom:	40 kA
Schlagweite:	2950 mm
Isolator:	Verbund-Langstabisolator
Ausführungsform:	CS160 C19L 1675/8400/3400
Kriechweg:	8400 mm
Verschmutzungsgrad:	II nach DIN EN 60071-2

Beachtung bei der Montage / Mengenermittlung

- 1) Verbindungsbolzen : Mutter und deren Sicherungen zum Mastschaft, zur niedrigeren Mastnummer oder nach unten
- 2) Brennstrebe : vom Mastschaft weg
- 3) Montage der Bauteile nach Herstellervorschrift
- 4) Montage der A2/A4 - Schraubenverbindungen gefettet
- 5) Pos.1: Größe Traggelenk anpassen an Mastkonstruktion
- 6) Feldabstandhalter: Einbau und Anzahl gemäß Schwingungsstudie
- 7) Länge und Einsatz variiert zwischen den Masten, Pos. 2+3 (Länge 0-700 mm Anzahl 0-2)

Index	Ausgabedatum	Name	Änderung
Techn. Referenz	erstellt von GSG-ECO Aschenbrenner	geprüft von GSG-BTL Winter	Erstelldatum 28.06.2018
Eigentümer der Zeichnung	Zugehörigkeit Bestand	Dokumentenart Anordnungszeichnung	Status Freigegeben
Identnummer 002-138-601	Titel 380-kV-DH-Kette, Verbund CS 160, 4x 264-AL1/34-ST1A und 4x243-AL1/39-ST1A 380/110-kV-Ltg. Karben - Großkrotzenburg		Objekt LH-11-3024
		Fremdnummer	Blatt