



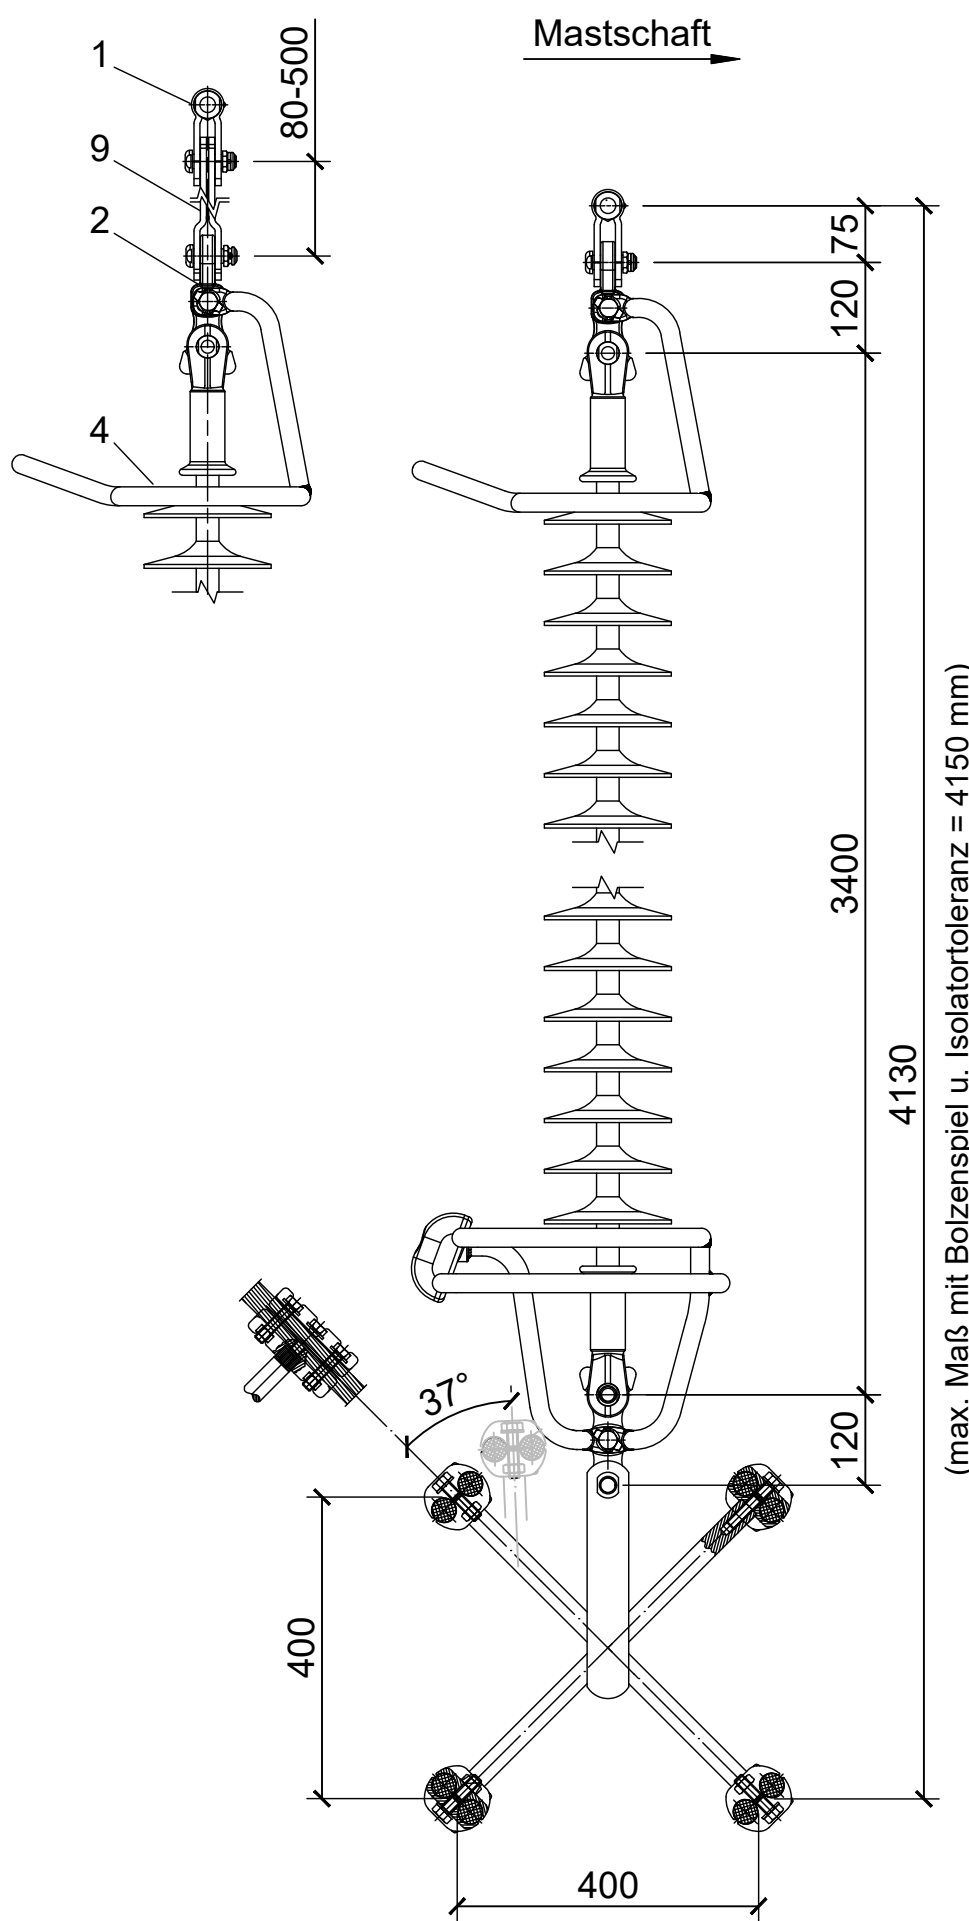

(max. Maß mit Bolzenspiel u. Isolator toleranz = 4150 mm)

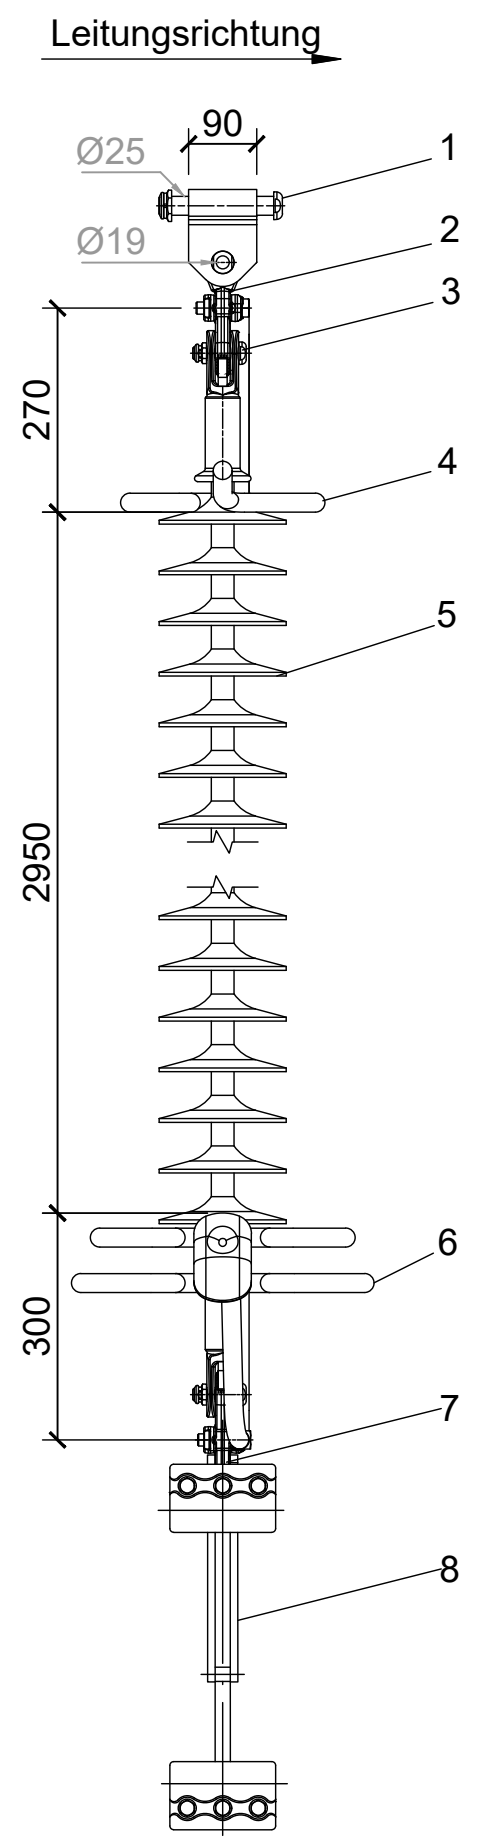

Stückliste

Pos. Nr.	Stück je Kette	Benennung	Nennkraft in kN	SAP - Nummer
1	1	Traggelenk DIN VDE 0212-466-A25X130-19-100 5)	200	52231510
2	1	Doppelöse D19 BH: 120 SAB Anschlag 41 GER	200	52219753
3	2	Verbindungsbolzen DIN VDE 0212-473-19X48-8.8	-	52232604
4	1	Schutzring Einhorn Verbund oben BH: 270	-	52201011
5	1	Isolator Verbund CS160 8400/3400 S19	160	52105323
6	1	Schutzring Tandem Verbund unten BH: 300	-	52201012
7	1	Doppelöse C19 BH: 120 SAB Anschlag 41	200	52219742
8	1	Stromschlaufendistanzhalter u. Lasche 4 BDL 21,1-23,4	-	52313120
9	1	Gabellasje DIN VDE 0212-478-A19-20 BH:80...500 6)	200	siehe Liste

Mechanische Werte

Kettengewicht:	ca. 60 kg
Kettenlänge:	ca. 4150 mm
Kettenfläche:	ca. 0,4 m²
Leiter:	4x243-AL1/39-ST1A 4x264-AL1/34-ST1A 4x243-AT1/39-A20SA 4x264-AT1/34-A20SA

Elektrische Werte

Bemessungs-Kurzzeitstrom:	40 kA
Schlagweite:	2950 mm
Isolator:	Verbund-Langstabisolator
Ausführungsform:	CS160 C19L 1675/8400/3400
Kriechweg:	8400 mm
Verschmutzungsgrad:	II nach DIN EN 60071-2: 1997
SPS-Klasse:	c nach IEC 60815

Beachtung bei der Montage / Mengenermittlung

- 1) Verbindungsbolzen: Mutter und deren Sicherungen zum Mastschaft, zur niedrigeren Mastnummer oder nach unten
- 2) Brennstrebe: vom Mastschaft weg
- 3) Montage der Bauteile nach Herstellervorschrift
- 4) Montage der A2/A4 - Schraubenverbindungen gefettet
- 5) Pos. 1: Größe Traggelenk anpassen an Mastkonstruktion
- 6) Pos. 9: Länge Gabellasje anpassen an Winkelstellung/Schlaufenführung

Index	Ausgabedatum	Name	Änderung		
Techn. Referenz		erstellt von GFG-DD-DO Aschenbrenner	geprüft von GFG-OC-HL Pultar	Erstelldatum 20.03.2025	Format A3-Q
					Maßstab 1:10
Eigentümer der Zeichnung Tennet Taking power further		Zugehörigkeit Bestand			Ausgabedatum
		Dokumentenart Anordnungszeichnung		Status In Erstellung	20.03.2025
		Titel Kettenzeichnung		Objekt LH-11-3024	
Identnummer 002-396-800		380-kV_EH-Kette SSDH_4x243/39 u. 4x264/34_Verbund_SPSc 380_110-kV Karben - Großkrotzenburg		Fremdnummer	Blatt