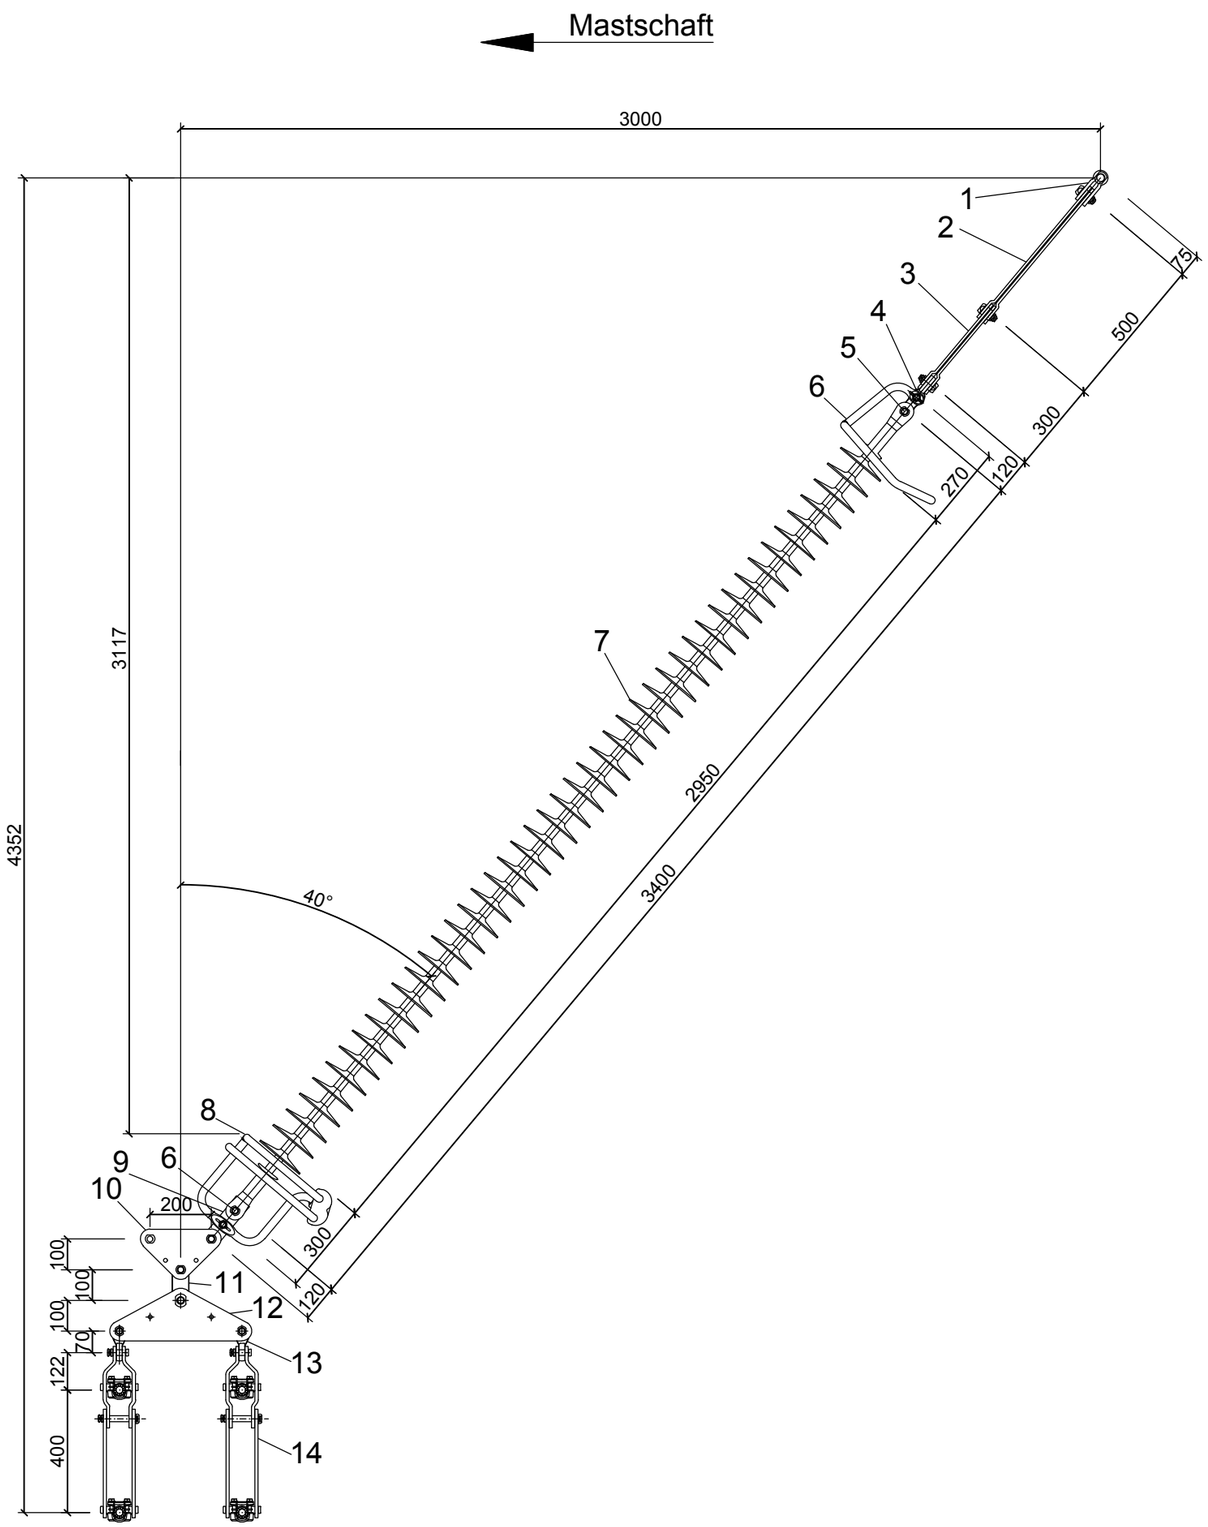


Stückliste

Pos. Nr.	Stück je Kette	Benennung	Nennkraft in kN	SAP - Nummer
1	2	Traggelenk DIN VDE 0212-466-A25x130...150-19-100	200	-
2	2	Gabellasche DIN VDE 0212-478-A19-20 BH: 500 5)	200	52223419
3	2	Gabellasche DIN VDE 0212-478-A19-20 BH: 300	200	52223415
4	2	Doppelöse D19 BH: 120 SAB Anschlag 41 GER	200	52219753
5	4	Verbindungsbolzen DIN VDE 0212-473-19x48-8.8	-	52232604
6	2	Schutzring Einhorn Verbund oben BH: 270	-	52201011
7	2	Isolator Verbund CS160 8400/3400 S19	160	52105323
8	2	Schutzring Tandem Verbund unten BH: 300	-	52201012
9	2	Doppelöse C19 BH: 120 SAB Anschlag 41	200	52219742
10	1	Abstandhalter A19-22-200/100 3ECK	280	52225543
11	1	Doppelöse A22 BH: 100	280	52219148
12	1	Abstandhalter A19-22-400/100 3ECK	280	52225577
13	2	Doppelöse DIN VDE 0212-469-B19 BH: 70	200	52219213
14	2	Spiraltragklemme S19 2-BDL 21,72-22,67	2x120	52301604

Mechanische Werte	
Kettengewicht:	ca. 125 kg
Kettenlänge:	ca. 4355 mm (bis Leiterachse)
Kettenfläche:	ca. 0,6 m²
Öffnungswinkel:	ca. 80°
Leiter:	243-AL1/39-ST1A 48 N/mm²
Eiszone / Windzone:	E1 / W1
Gewicht-/ Windspannweite:	500 / 400 m

Elektrische Werte	
Nennkurzzeitstrom:	40 kA
Schlagweite:	2950 mm
Isolator:	Verbund-Langstabisolator
Ausführungsform:	CS160 C19L 1675/8400/3400
Kriechweg:	8400 mm
Verschmutzungsgrad:	II nach DIN EN 60071-2

Beachtung bei der Montage / Mengenermittlung

1) Verbindungsbolzen : Mutter und deren Sicherungen zum Mastschaft, zur niedrigeren Mastnummer oder nach unten
2) Brennstrebe : nach außen
3) Montage der Bauteile nach Herstellervorschrift
4) Montage der A2/A4 - Schraubenverbindungen gefettet
5) entfällt auf Traverse 2 bei dem V-Strang mit Unterkonstruktion

Mast 78 und 79, linkes System

Index	Ausgabedatum	Name	Änderung

Techn. Referenz	erstellt von: GSG-ECO Aschenbrenner	geprüft von: GSG-BTL Winter	Erstelldatum: 17.09.2018	Format: A3-Q Maßstab: 1:20
Eigentümer der Zeichnung: TenneT Taking power further	Zugehörigkeit: Vorplanung Dokumentenart: Anordnungszeichnung Status: In Erstellung			Ausgabedatum: 04.10.2018
Identnummer: 002-144-374	Titel: 380-kV-V-Kette Verbundisolatoren 243-AL1/39-ST1A 4-er Bündel 380_110-kV Karben - Großkrotzenburg		Objekt: LH-11-3024 Fremdnummer:	Blatt: